


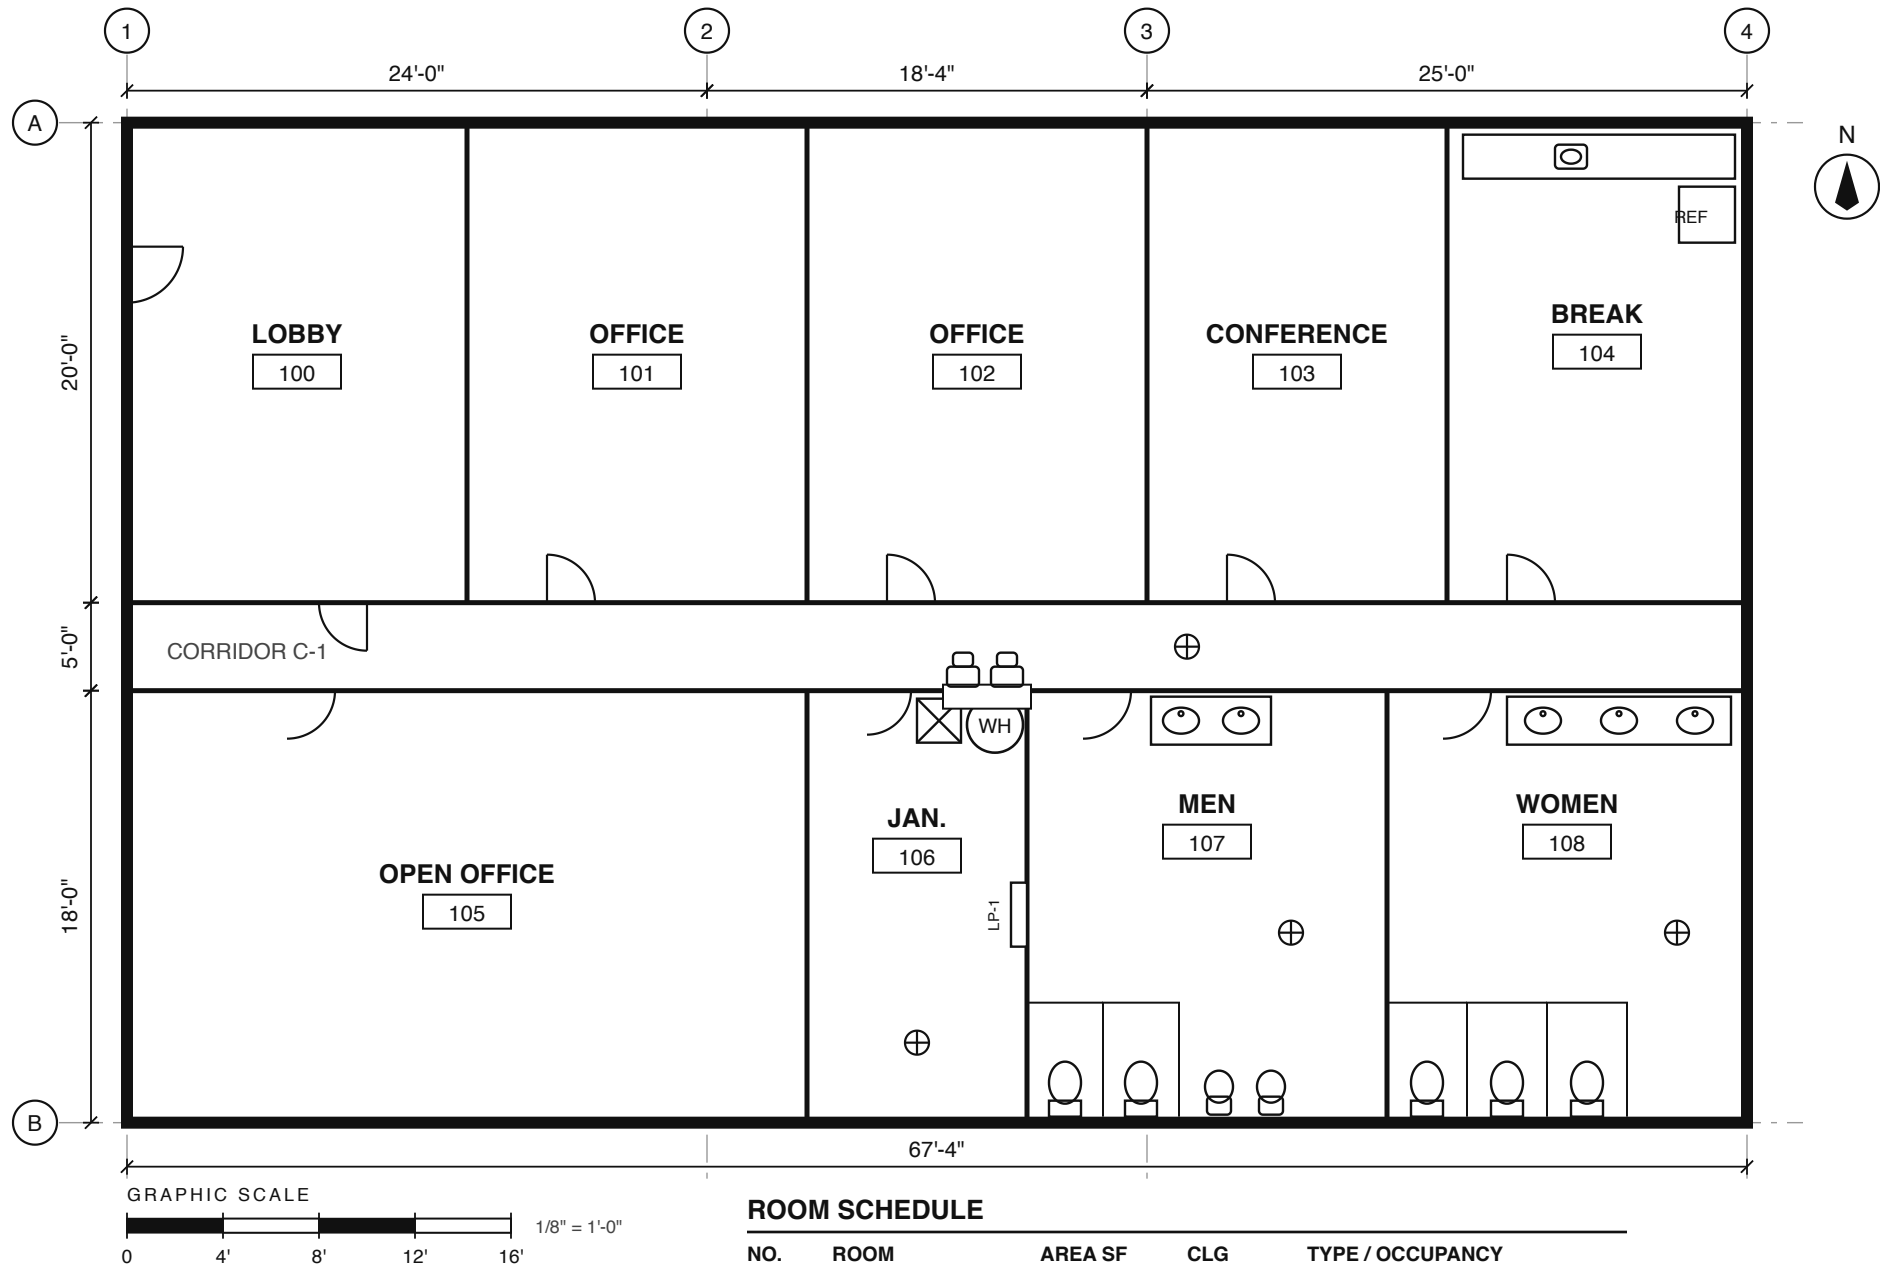

ROOM SCHEDULE				
NO.	ROOM	AREA SF	CLG	TYPE / OCCUPANCY
100	LOBBY	283	9'-0"	LOBBY
101	OFFICE	283	9'-0"	OFFICE
102	OFFICE	283	9'-0"	OFFICE
103	CONFERENCE	250	9'-0"	CONFERENCE
104	BREAK	250	9'-0"	BREAK
105	OPEN OFFICE	510	9'-0"	OFFICE
106	JAN.	165	8'-0"	STORAGE / MECH
107	MEN	270	8'-0"	RESTROOM, PUBLIC
108	WOMEN	270	8'-0"	RESTROOM, PUBLIC
C-1	CORRIDOR	337	8'-0"	CIRCULATION

DECK 12'-0" A.F.F. TYP. · MEP DESIGN-BUILD, SEE NOTE 6

GENERAL NOTES

1. ALL DIMENSIONS TO FACE OF STUD UNLESS NOTED OTHERWISE.
2. VERIFY ALL FIXTURE ROUGH-INS WITH PLUMBING PLANS.
3. PROVIDE ADA CLEARANCES AT ALL RESTROOM FIXTURES.
4. FD = FLOOR DRAIN, SLOPE 1/4" PER FOOT TO DRAIN, TYP.
5. WH = 50 GAL ELECTRIC WATER HEATER ON 18" STAND.
6. MEP DESIGN-BUILD BY CONTRACTOR: SIZE AND ROUTE PER CODE.
7. RTU-1, 2,000 CFM, ON ROOF OVER JAN. 106; DUCT BY D-B CONTRACTOR.
8. PANEL LP-1, 42 POLE, IN JAN. 106.
9. WATER SERVICE + GAS METER AT THE JAN. 106 EXTERIOR WALL.

LEGEND

- FLOOR DRAIN
- WATER HEATER
- MOP SINK
- DRINKING FOUNTAIN

COUNTTOOLING — SAMPLE PLAN

PROJECT	SUITE 200 OFFICE TI	SHEET	
SCALE	DATE	A-101	
1/8" = 1'-0"	07/31/26		
FIRST FLOOR PLAN	DRAWN: CT		