


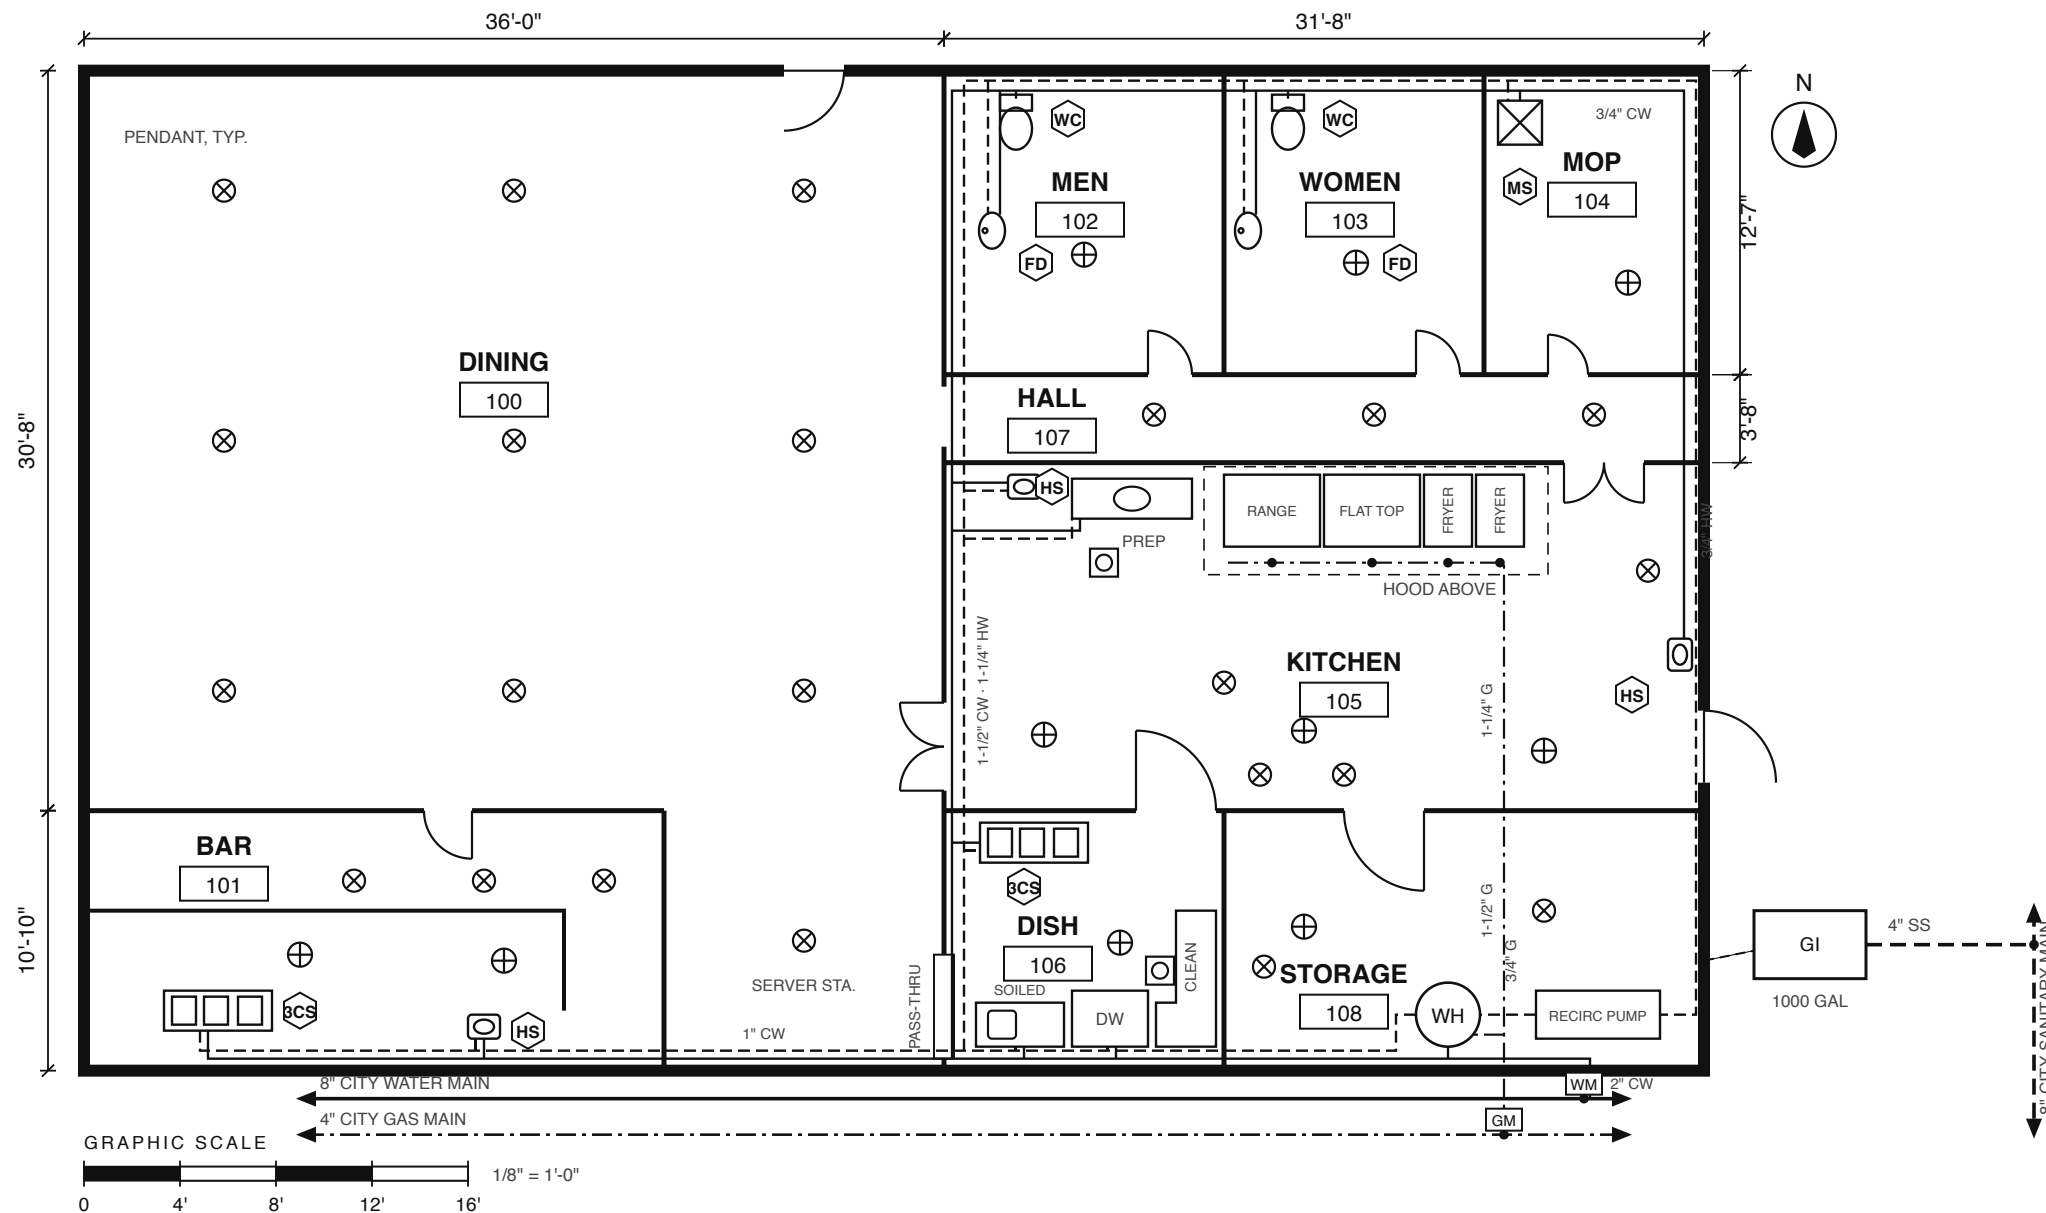

PLUMBING KEYNOTES

- WC WATER CLOSET, FLOOR MTD
- HS HAND SINK, WALL HUNG
- 3CS 3-COMPARTMENT SINK
- MS MOP SINK, FLOOR MTD
- FD FLOOR DRAIN W/ TRAP PRIMER, TYP.
- FS FLOOR SINK, 1/2 GRATE
- DW COMMERCIAL DISHWASHER, INDIRECT WASTE TO FS
- GI GREASE INTERCEPTOR, 1000 GAL, EXTERIOR
- WH WATER HEATER, 100 GAL GAS
- RP RECIRC PUMP ON THE HW RETURN
- SS SANITARY SEWER TO CITY
- W DOMESTIC WATER FROM CITY
- G GAS SERVICE FROM CITY

ALL KITCHEN WASTE THROUGH GREASE INTERCEPTOR, TYP.

LEGEND

- CW DOMESTIC COLD WATER
- HW DOMESTIC HOT WATER
- G GAS
- SS SANITARY SEWER
- GAS DROP W/ SHUTOFF, TYP.
- LIGHT FIXTURE, TYP.



COUNTTOOLING — SAMPLE PLAN

PROJECT MAIN ST RESTAURANT

SHEET




SCALE
1/8" = 1'-0"

DATE
07/31/26

PLUMBING PLAN

DRAWN: CT


P-101

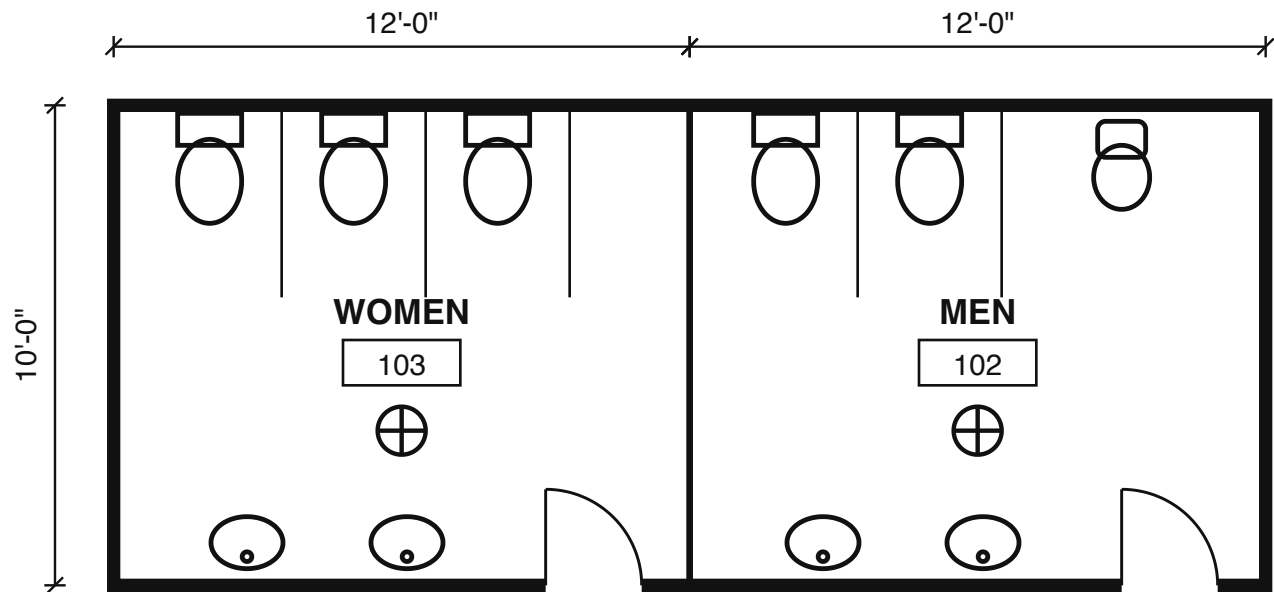

1 ENLARGED RESTROOM PLAN
SCALE: 1/4" = 1'-0"

SHEET NOTES

1. PLAN 1 IS DRAWN AT 1/4" = 1'-0". DETAIL 2 IS DRAWN AT 1/2" = 1'-0".
2. PROVIDE DETAIL 2 AT EACH OF (4) COOK LINE AND BAR STATIONS.
3. FLOOR DRAINS W/ TRAP PRIMER, TYP.
4. ALL DIMENSIONS TO FACE OF FINISH.

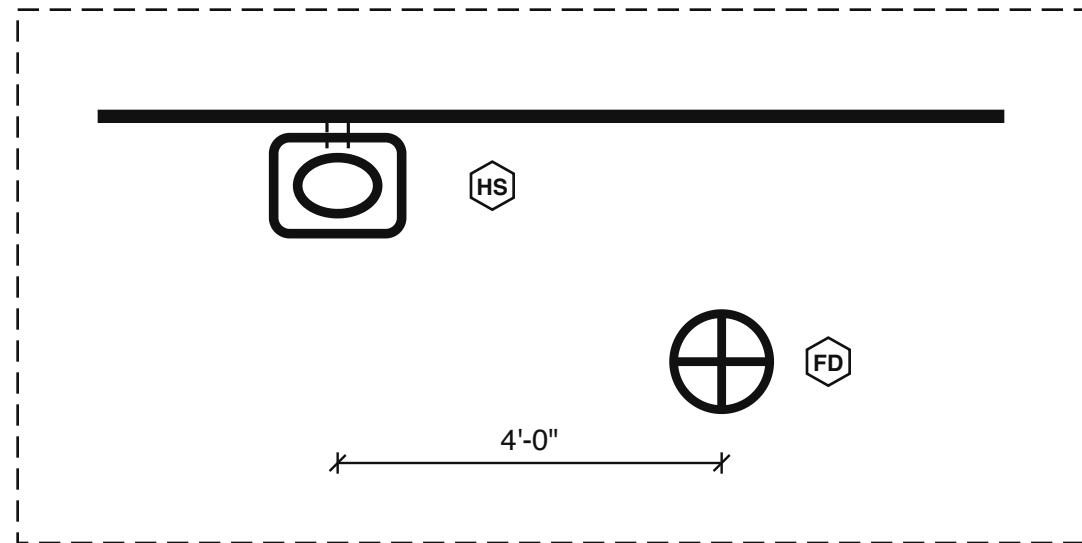

2 HAND SINK STATION · TYP. OF 4
SCALE: 1/2" = 1'-0"



COUNTTOOLING — SAMPLE PLAN

PROJECT MAIN ST RESTAURANT

SHEET



SCALE
AS NOTED

DATE
07/31/26

ENLARGED PLANS

DRAWN: CT

P-401

PLUMBING FIXTURE SCHEDULE

TAG	FIXTURE	CW	HW	W	V
WC-1	WATER CLOSET, FLOOR MTD, FLUSH VALVE	1"	-	4"	2"
U-1	URINAL, WALL HUNG, FLUSH VALVE	3/4"	-	2"	1-1/2"
L-1	LAVATORY, COUNTER MTD	1/2"	1/2"	1-1/2"	1-1/4"
HS-1	HAND SINK, WALL HUNG	1/2"	1/2"	1-1/2"	1-1/4"
3CS-1	3-COMPARTMENT SINK	3/4"	3/4"	2"	1-1/2"
MS-1	MOP SINK, FLOOR MTD	3/4"	3/4"	3"	2"
FD-1	FLOOR DRAIN W/ TRAP PRIMER	1/2"	-	3"	2"
FS-1	FLOOR SINK, 1/2 GRATE	-	-	3"	2"

SCHEDULE NOTES

1. ROUGH-IN SIZES ARE MINIMUMS; SEE PLANS FOR RUN SIZES.
2. ALL FIXTURES ADA WHERE SHOWN ON THE ARCHITECTURAL PLANS.

COUNTTOOLING — SAMPLE PLAN		
PROJECT	MAIN ST RESTAURANT	
SCALE	DATE	
NONE	07/31/26	
SCHEDULES	DRAWN: CT	
		P-501